

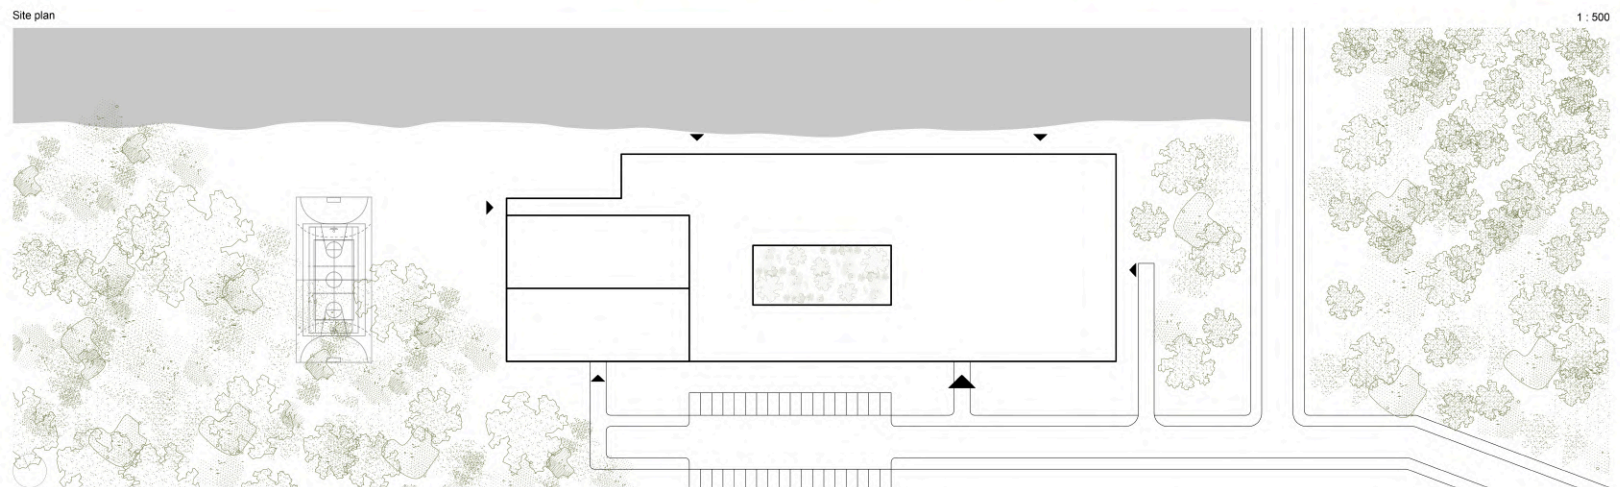


PORT PRASKI HIGH SCHOOL

Initially a sports oriented high school, yet came to life as something way more valuable and versatile. Low stimulating environment for neurodivergent students, broad spaces for comfortable social interactions, enclosed privacy and protection from the whole city, specialized rooms for advanced physical enhancement...

A single place, where education pays attention on your health, wellness of the mind and the peace of your soul.

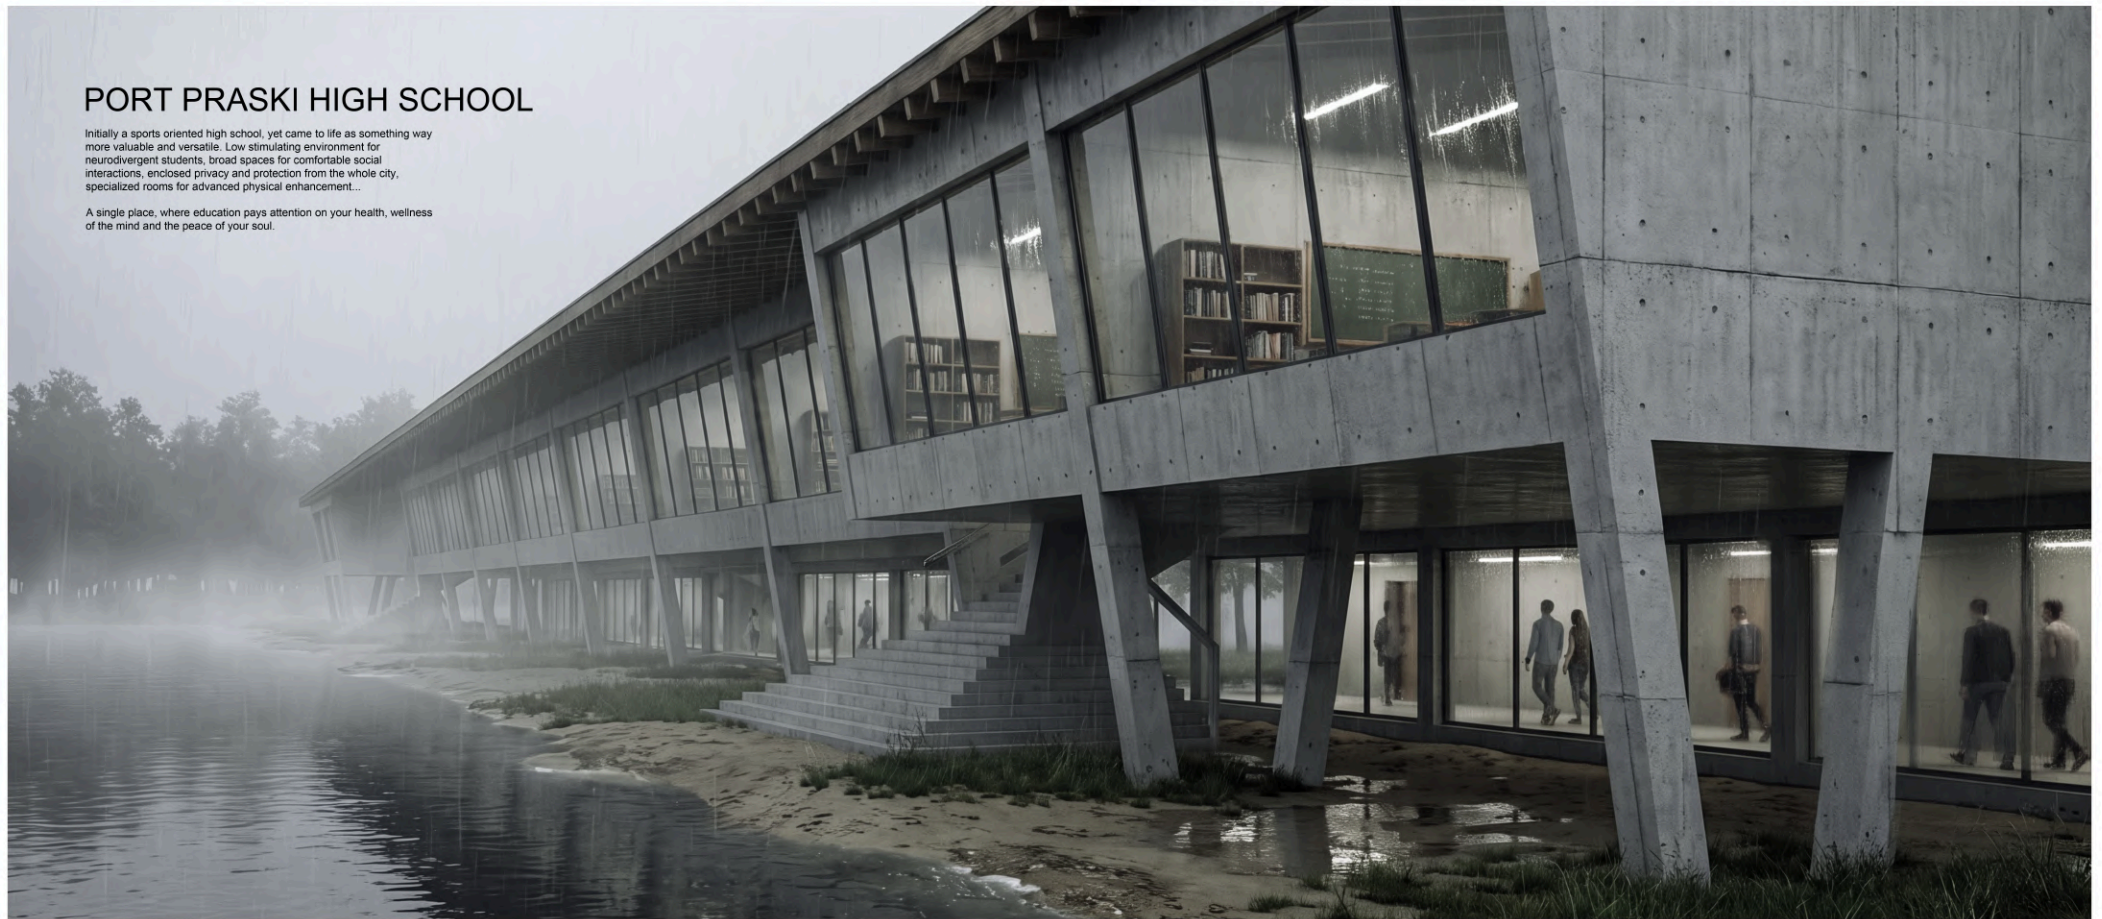


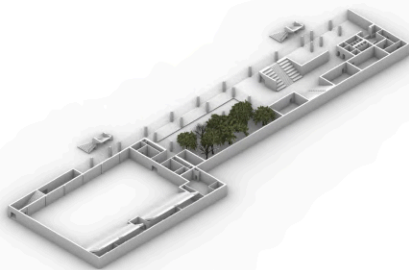

Ground Floor Plan



1 : 200

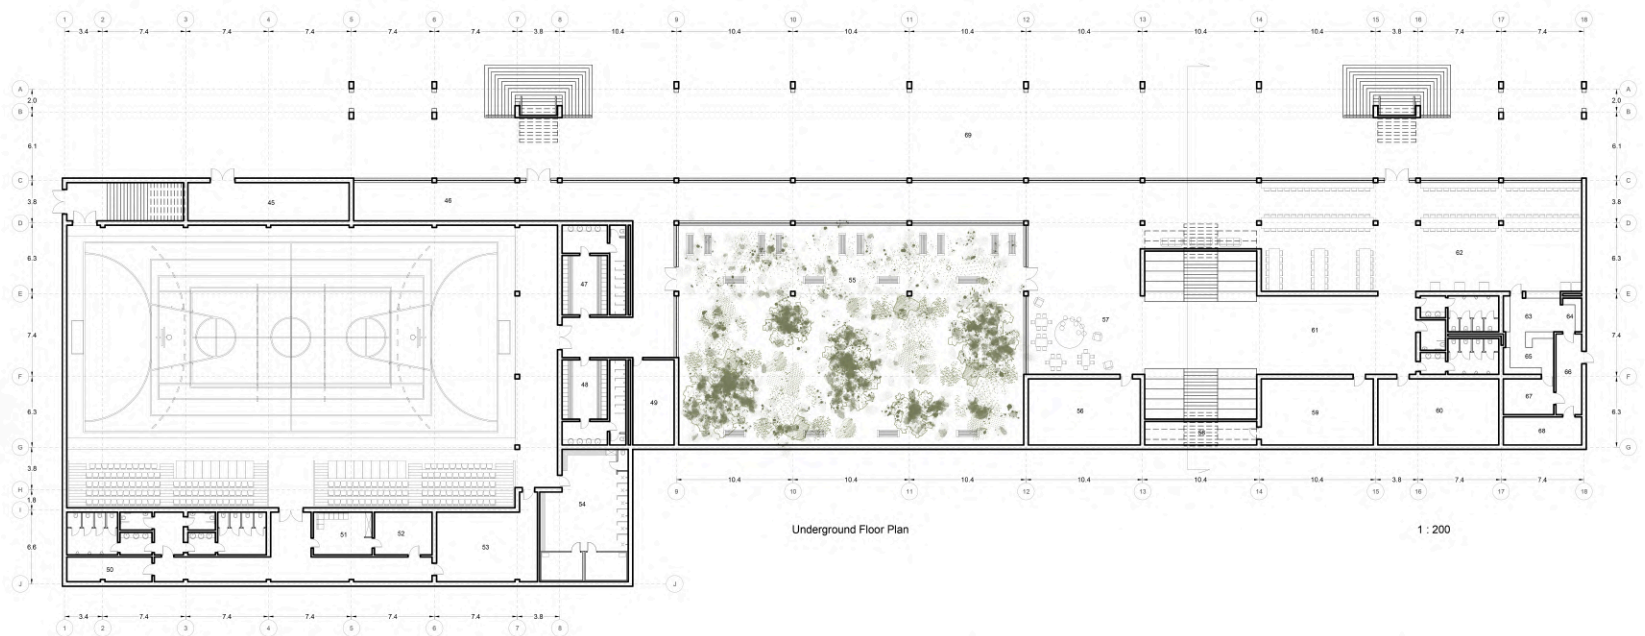

Underground Floor Plan

1 : 200

